

승강기 사양

호 기	2호기	3호기
용 도	승객용,장애인용	승객용
구 동 방 식	기계실 없는 엘리베이터 (MRL)	
적 재 용 량	12인승 (900 kg)	
운 전 방 식	2대 병렬 군관리 운전	
제 어 방 식	VVV - F	
운 행 속 도	90 M/MIN	
운 행 층 수	B6F~12F (18FL/18SF)	
행 정 거 리	57600 mm	
출입문 구동방식	2 PANEL CENTER OPEN	
카 크기(INSIDE)	W1300 x D1600	
출입문 크기	W900 x H2100	
비상정지장치	GOVERNOR	
방화도어	전층 적용	
건물측 입력전원	Ø3 - 380 - 60 HZ	
제 어 회 로	DC 24 V	
신 호 회 로	DC 24 V	
조 명 회 로	Ø1 - 220 - 60 HZ	

재사용 자재 설치 방법

부 품 명		재사용 여부		작업 조건
		3호기	3호기	
가이드 레일	카측	O	O	기존 가이드레일 이설
	균형추측	X	X	가이드레일 신설
레일 브래킷	카측	X	X	레일 이설로 브래킷 재설치
	균형추측	X	X	레일 이설로 브래킷 재설치
권상기 기계대		X	X	설치방법의 차이로 신설이 필요함
완충기 받침대		X	X	기존 완충기 받침대 무효화 조건
삼방틀		O	O	덧씩우기 작업
승강장 문턱		X	X	전층 문턱 교체 조건
균형추		X	X	설계구조 차이로 전부 교체


승강기 공급범위

1. 엘리베이터 제작 및 설치공사
2. 기존 승강기 철거공사 및 고철물 매각
3. 카측 가이드레일 이설공사(업체의 설계구조 반영조건)
4. 균형추측 가이드레일 신설공사(업체의 설계구조 반영조건)
5. MRL 타입의 승강로 정상부의 기계대 신설(업체의 설계구조 반영조건)
6. 기존 삼방틀 덧씩우기 작업
7. 최상층 제어반 박스 재사용 조건이고, 업체의 설계 및 설치 구조상 박스의 재사용이 불가 하여 벽체의 콘크리트를 파쇄할 경우에는 수급자가 구조검토 및 마감공사를 하는 조건
8. 카 내부 LCD 21.5인치 신설
9. 카 내부 기존 CCTV 카메라 철거후 400만화소 신설(결선 및 테스트 포함)
10. 카 내부 에어컨 증발식 설치
11. 기존 분전반 교체공사(2021.01.01. 한국전기설비규정)
12. 법적 조도 확보를 위한 LED 조명등 신설공사(검사방법 표준화 기준)
13. 피트 완충기 철거 및 교체공사
14. 기존 승장문턱 철거 및 신설(검사방법 표준화 기준, 재료분리대 포함)
15. 공사 도중의 자재반입 통로에 대한 보양 작업
16. 기계실 비상통화장치 철거 및 신설(검사방법 표준화 기준)
17. 승강기 설치공사와 관련한 철물, 배관, 배선, 결선공사 일체
18. 공사중 1층 승강장 출입문 앞의 안전부스 설치
19. 건축 구조물 훼손 시에 원상복구 공사
20. 승강기 국내외 제작공장 검수 비용 일체
21. 한국승강기안전공단 설치검사(재검사 비용 포함) 비용 일체
22. 설치완료 후, 승강로, 피트, 카의 청결상태 확보
23. 피트부 무근 타설 및 에폭시 도장 작업
24. 그 외 시방서 및 계약서에서 규정한 세부사항과 시공범위 조건 적용

주 기

- 승강기 업체 선정 후 승강기 공급업체의 상세도면에 기준하여 설치할 것.
- 선정된 승강기 업체는 현장 실측 후 설치 도면 작성할 것.


CUSTOMER		한국정보통신진흥협회			
UNIT	MM	SCALE	NONE	PROJECT TITLE	한국정보통신진흥협회
DRWN	DEND	CHKD	APPD		
강 연 진				DRAWING NO.	-
		DWG. DATE 26.07.06		DRAWING TITLE	승강기 사양 및 공급범위
		CAD NAME			

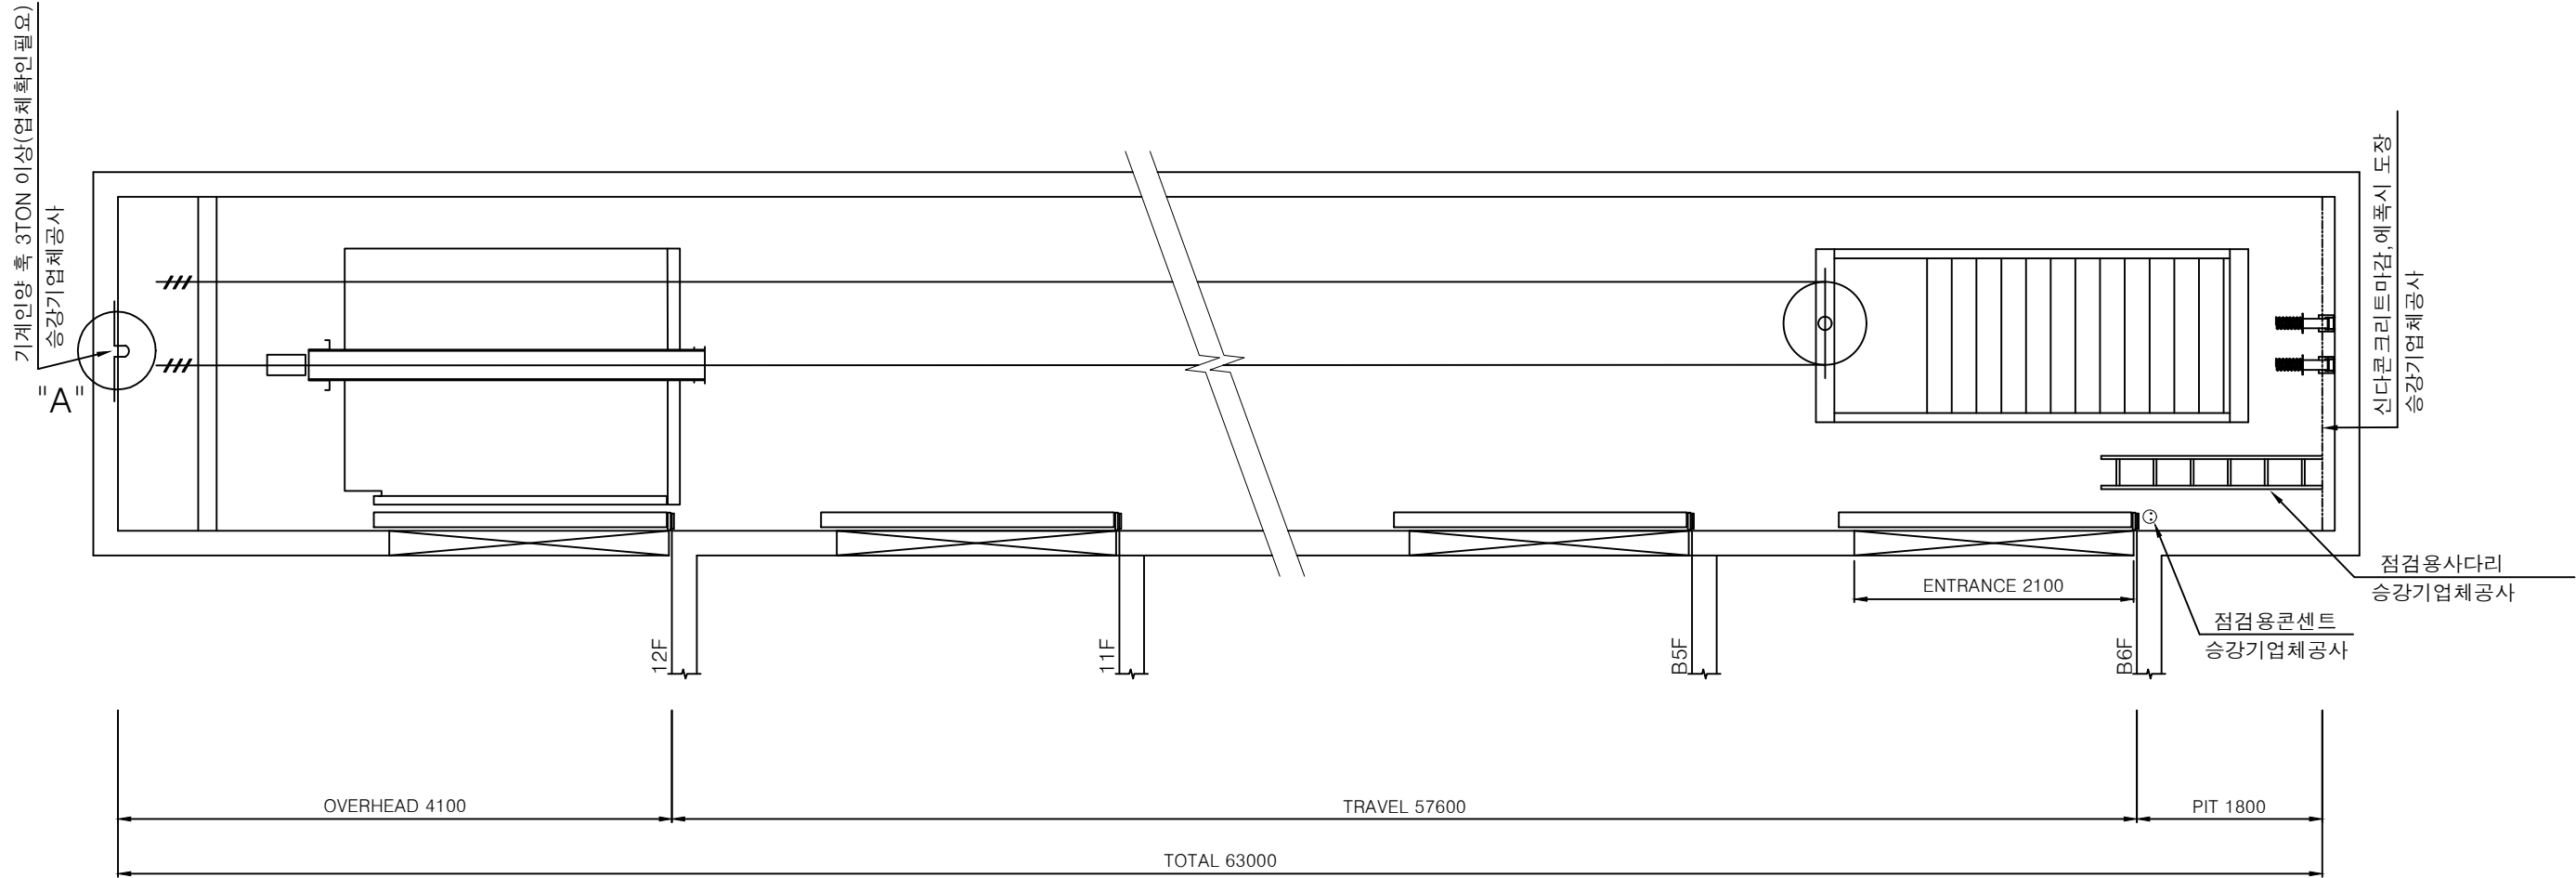

[참고]

PIT	B6F	B5F	B4F	B3F	B2F	B1F	1F	2F	3F
1800	3400	3400	3900	3400	3400	3700	3900	3200	3200
4F	5F	6F	7F	8F	9F	10F	11F	OH	
3200	3200	3200	3200	3200	3200	3200	3200	4100	

호기	#1, #2
용도	승객용, 장애인용
인승	12인승
정격하중	900 kg
운행층	B6~12F(18FL/18SF)
정격속도	90 m/min
운전방식	2대 그룹 운전
구동방식	MRL

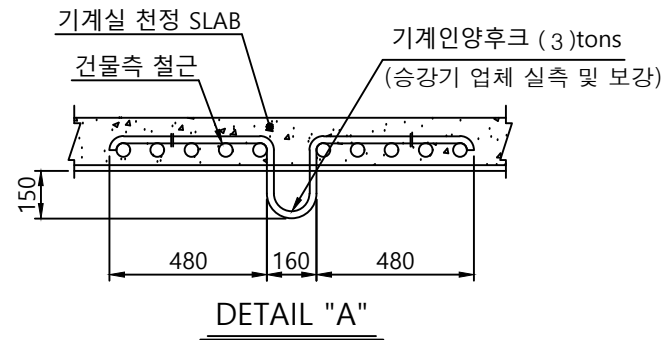


승강로 단면도 (#2,#3)

SCALE : 1/70 (A3)


주 기

- 승강기 업체 선정 후 승강기 공급업체의 상세도면에 기준하여 설치할 것.
- 선정된 승강기 업체는 현장 실측 후 설치 도면 작성할 것.


CUSTOMER		한국정보통신진흥협회			
UNIT	MM	SCALE	NONE	PROJECT TITLE	한국정보통신진흥협회
DRWN	DEND	CHKD	APPD		
강 연 진				DRAWING NO.	-
 GLS		DWG. DATE 26.07.06		DRAWING TITLE	승강로 단면도 (2~3호기)
		CAD NAME			

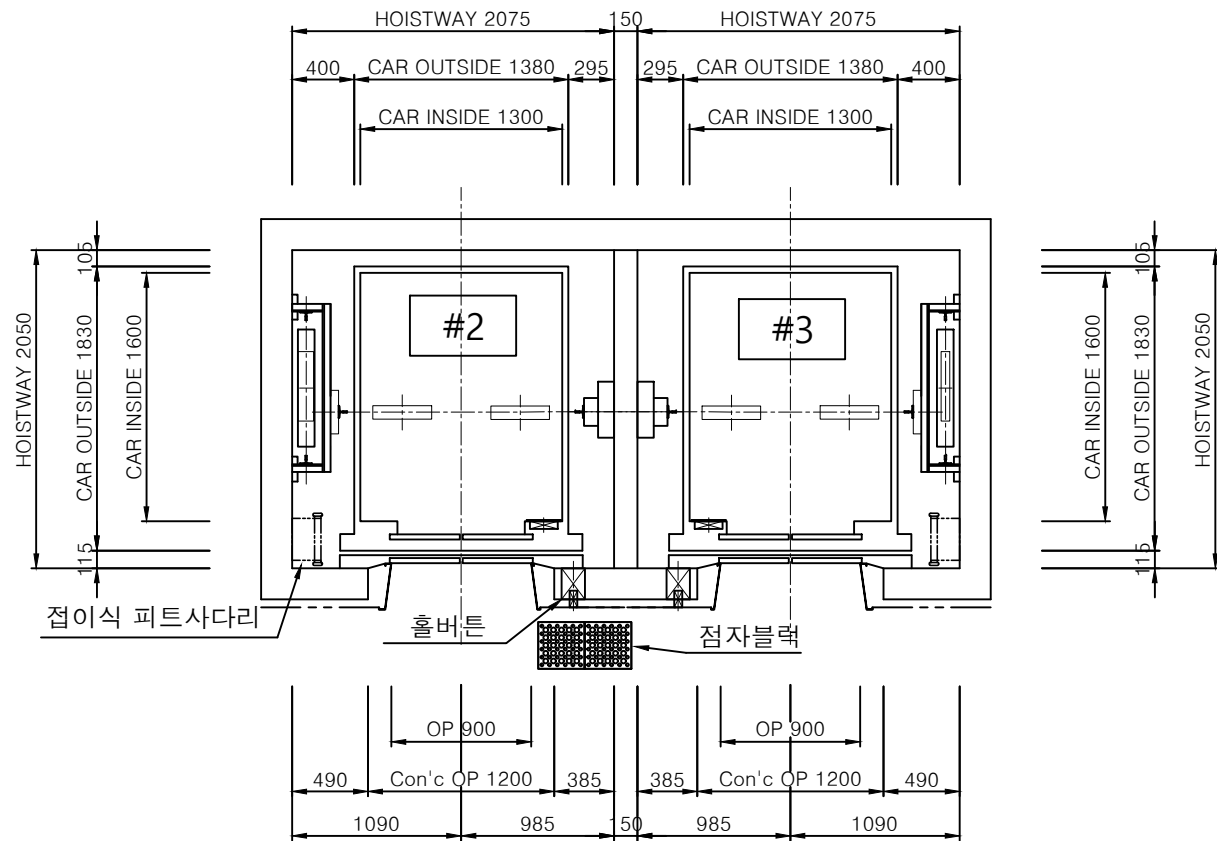

기타층

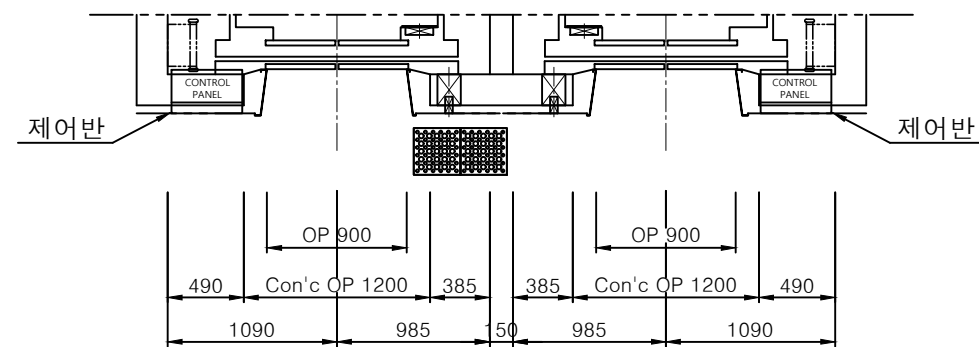

12층

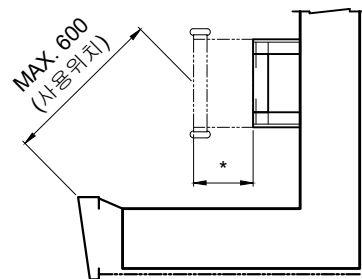

접이식 피트 사다리

승강로 평면도 (#2,#3)


SCALE : 1/50 (A3)

호 기	#1, #2
용 도	승객용, 장애인용
인 승	12인승
정격하중	900 kg
운행층	B6~12F(18FL/18SF)
정격속도	90 m/min
운전방식	2대 그룹 운전
구동방식	MRL


주 기

1. 승강기 업체 선정 후 승강기 공급업체의 상세도면에 기준하여 설치할 것.
2. 선정된 승강기 업체는 현장 실측 후 설치 도면 작성할 것.


CUSTOMER		한국정보통신진흥협회			
UNIT	MM	SCALE	NONE	PROJECT	한국정보통신진흥협회
DRWN	DEND	CHKD	APPD	TITLE	
강 연 진				DRAWING NO.	—
 GLS		DWG. DATE 26.07.06		DRAWING TITLE	승강로 평면도 (2~3호기)
		CAD NAME			

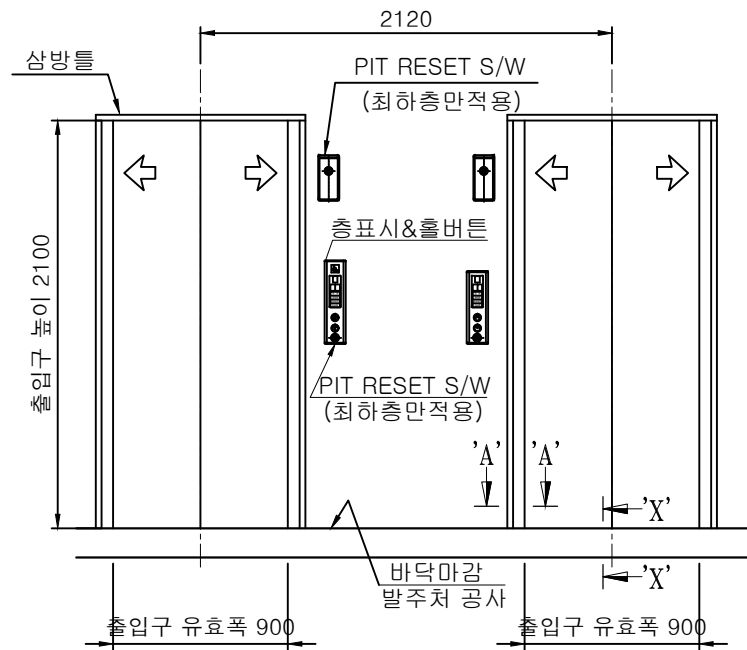


B6층~B2층

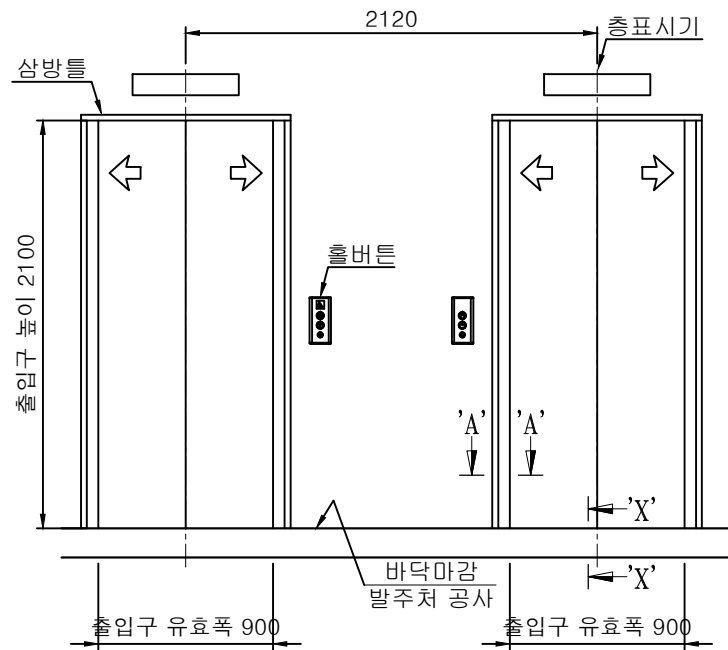


1층

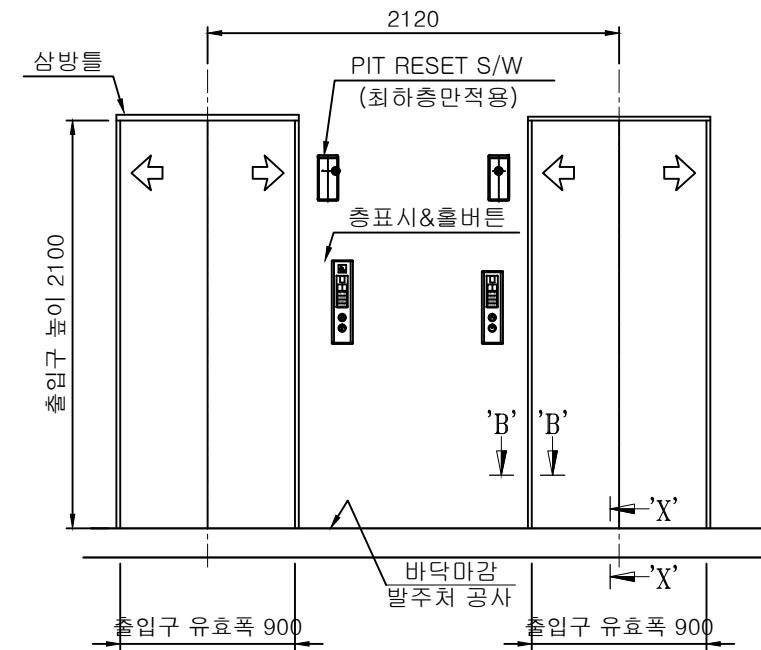


기타층

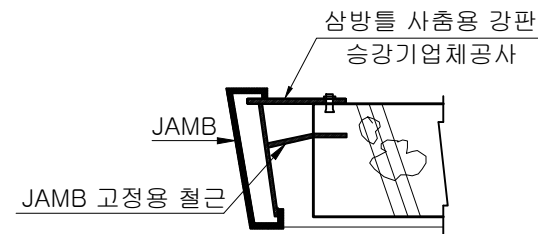

SEC "A-A"

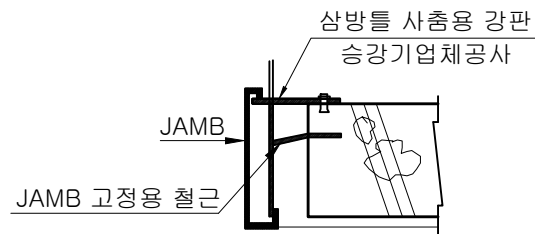

SEC "B-B"

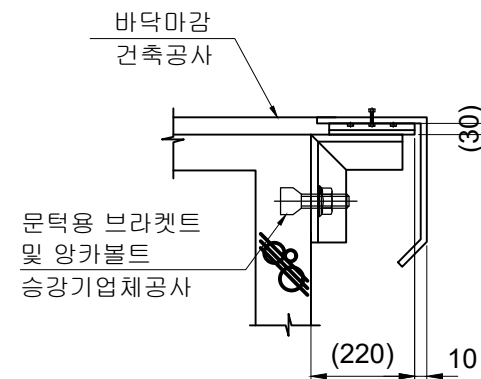

SEC "X-X"

출입구 정면도 (#2,#3)

SCALE : 1/40 (A3)

주기

1. 승강기 업체 선정 후 승강기 공급업체의 상세도면에 기준하여 설치할 것.
2. 선정된 승강기 업체는 현장 실측 후 설치 도면 작성할 것.

CUSTOMER		한국정보통신진흥협회			
UNIT	MM	SCALE	NONE	PROJECT	한국정보통신진흥협회
DRWN	DEND	CHKD	APPD	TITLE	
강 연 진				DRAWING NO.	-
 GLS		DWG. DATE 26.07.06		DRAWING TITLE	출입구 정면도(2~3호기)
		CAD NAME			